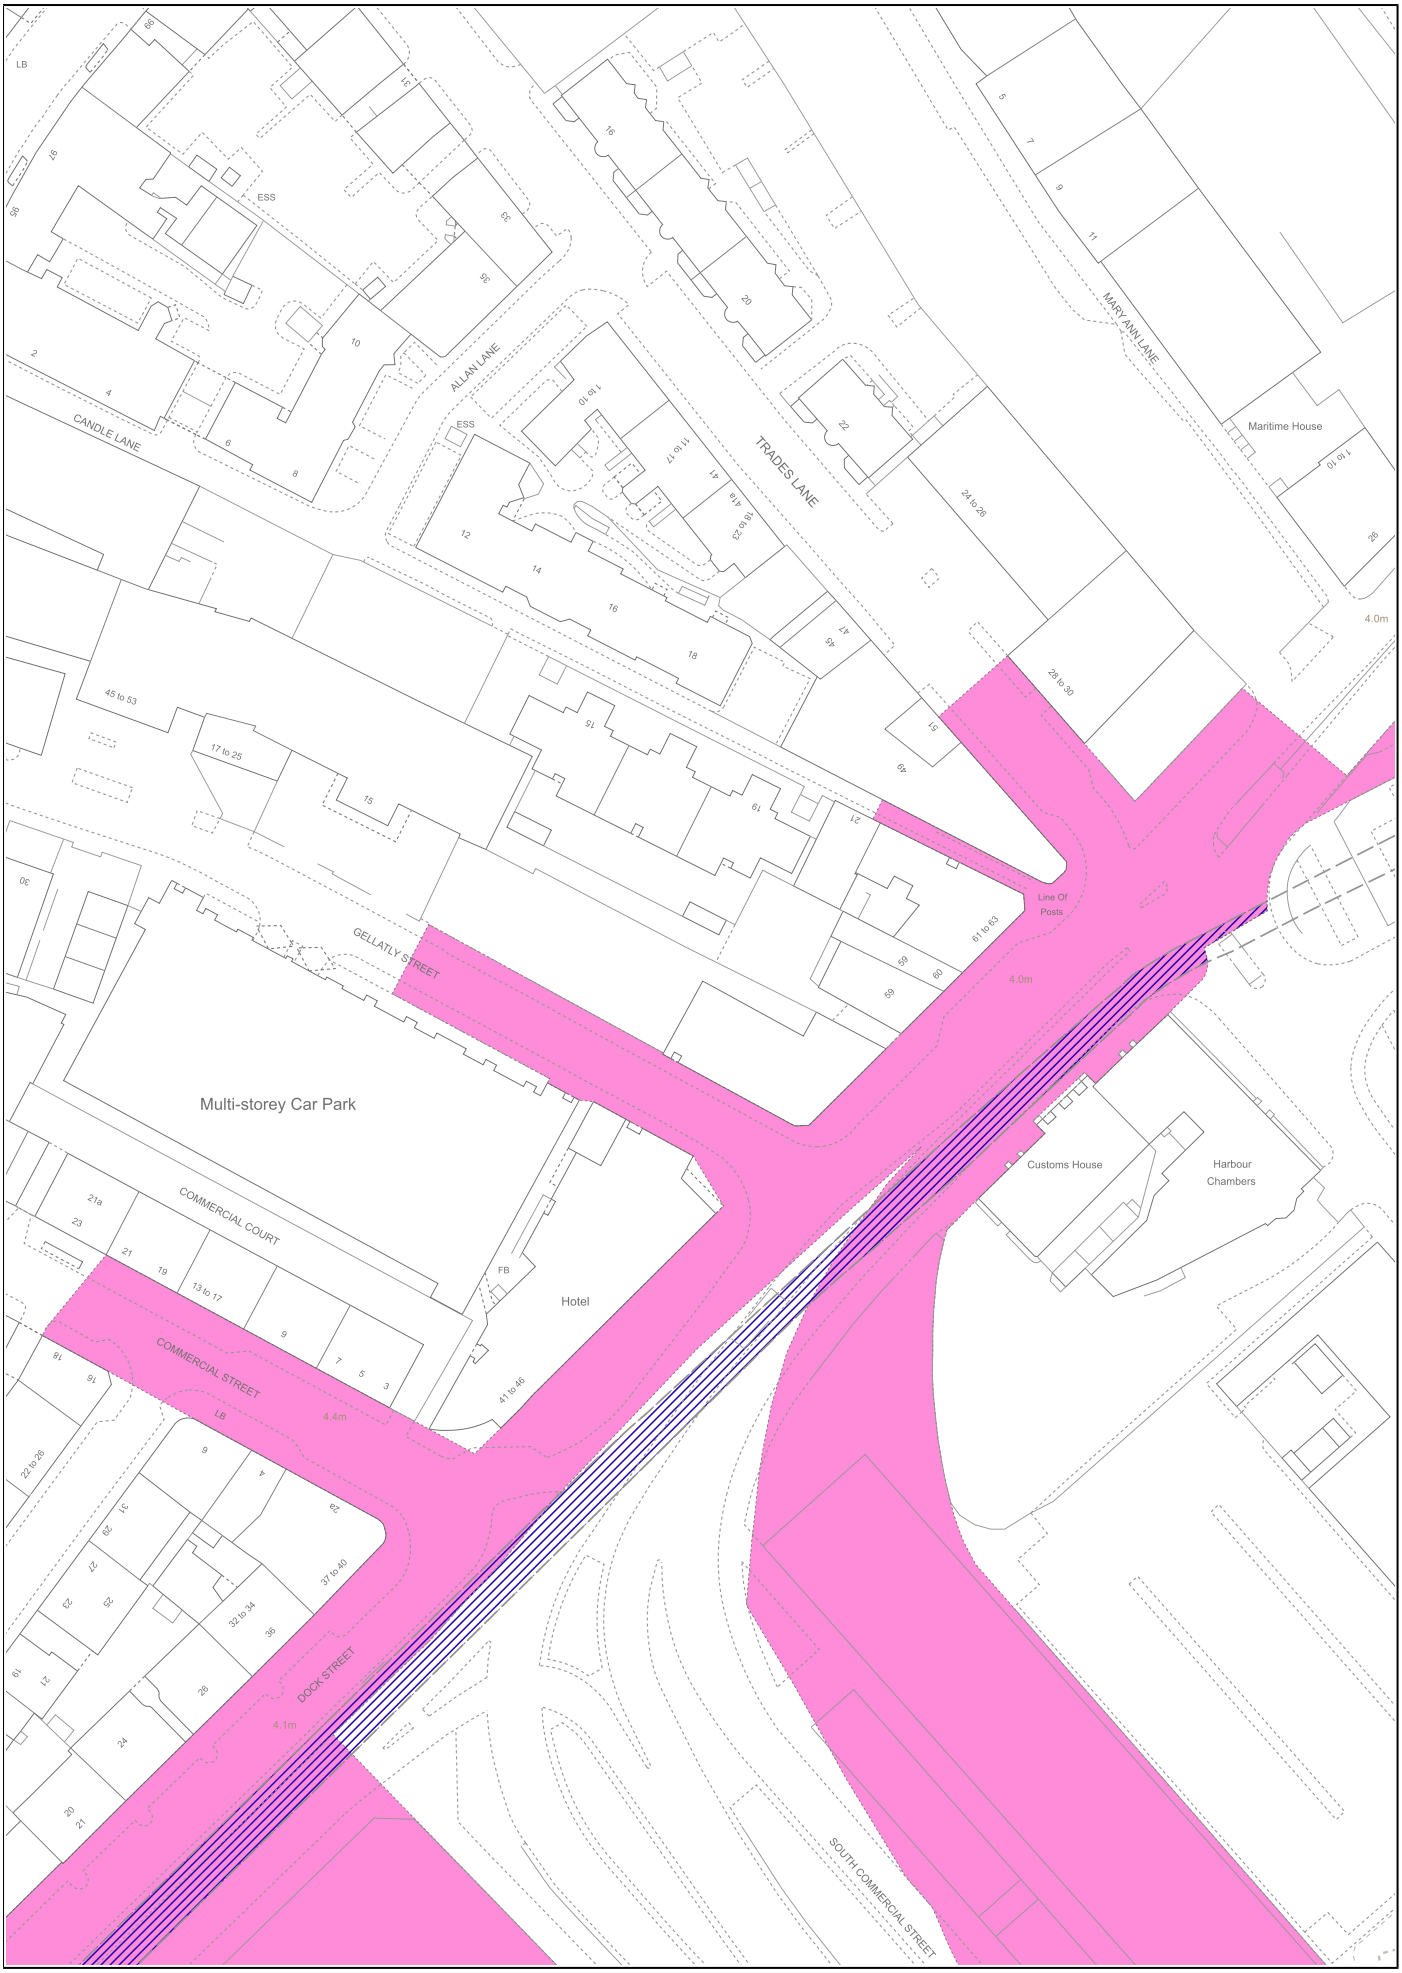
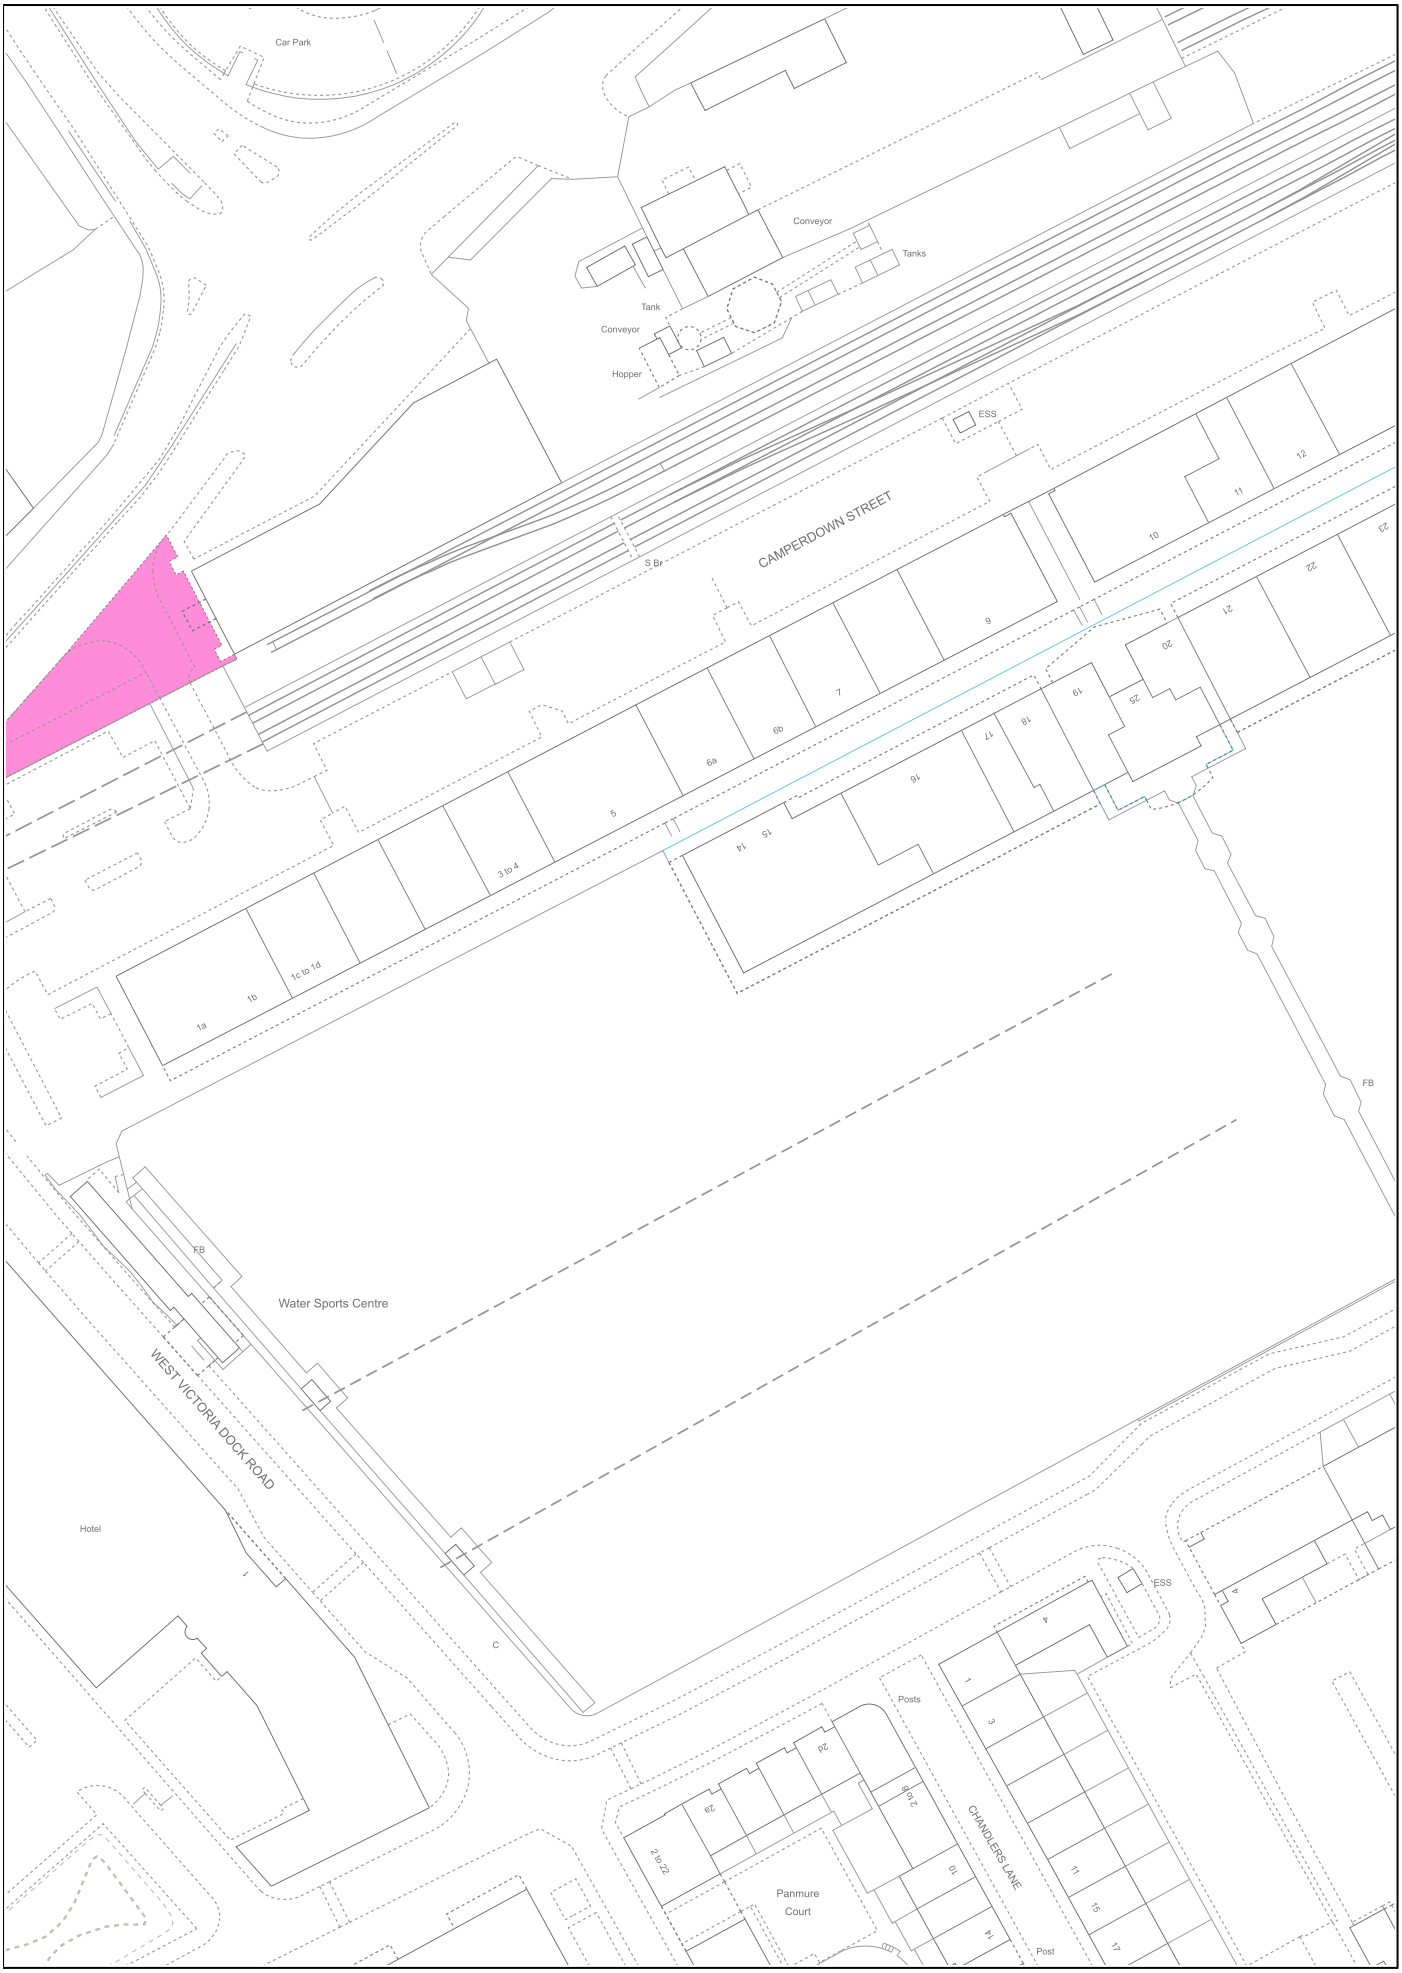
LAND REGISTER OF SCOTLAND	Version date	TITLE NUMBER
	28/10/2025	**ANG36283**
N	BRITISH NATIONAL GRID EASTING/NORTHING	50m
340549, 729973	Survey Scale: 1:1250	Print Scale: 1:1250 @ A4

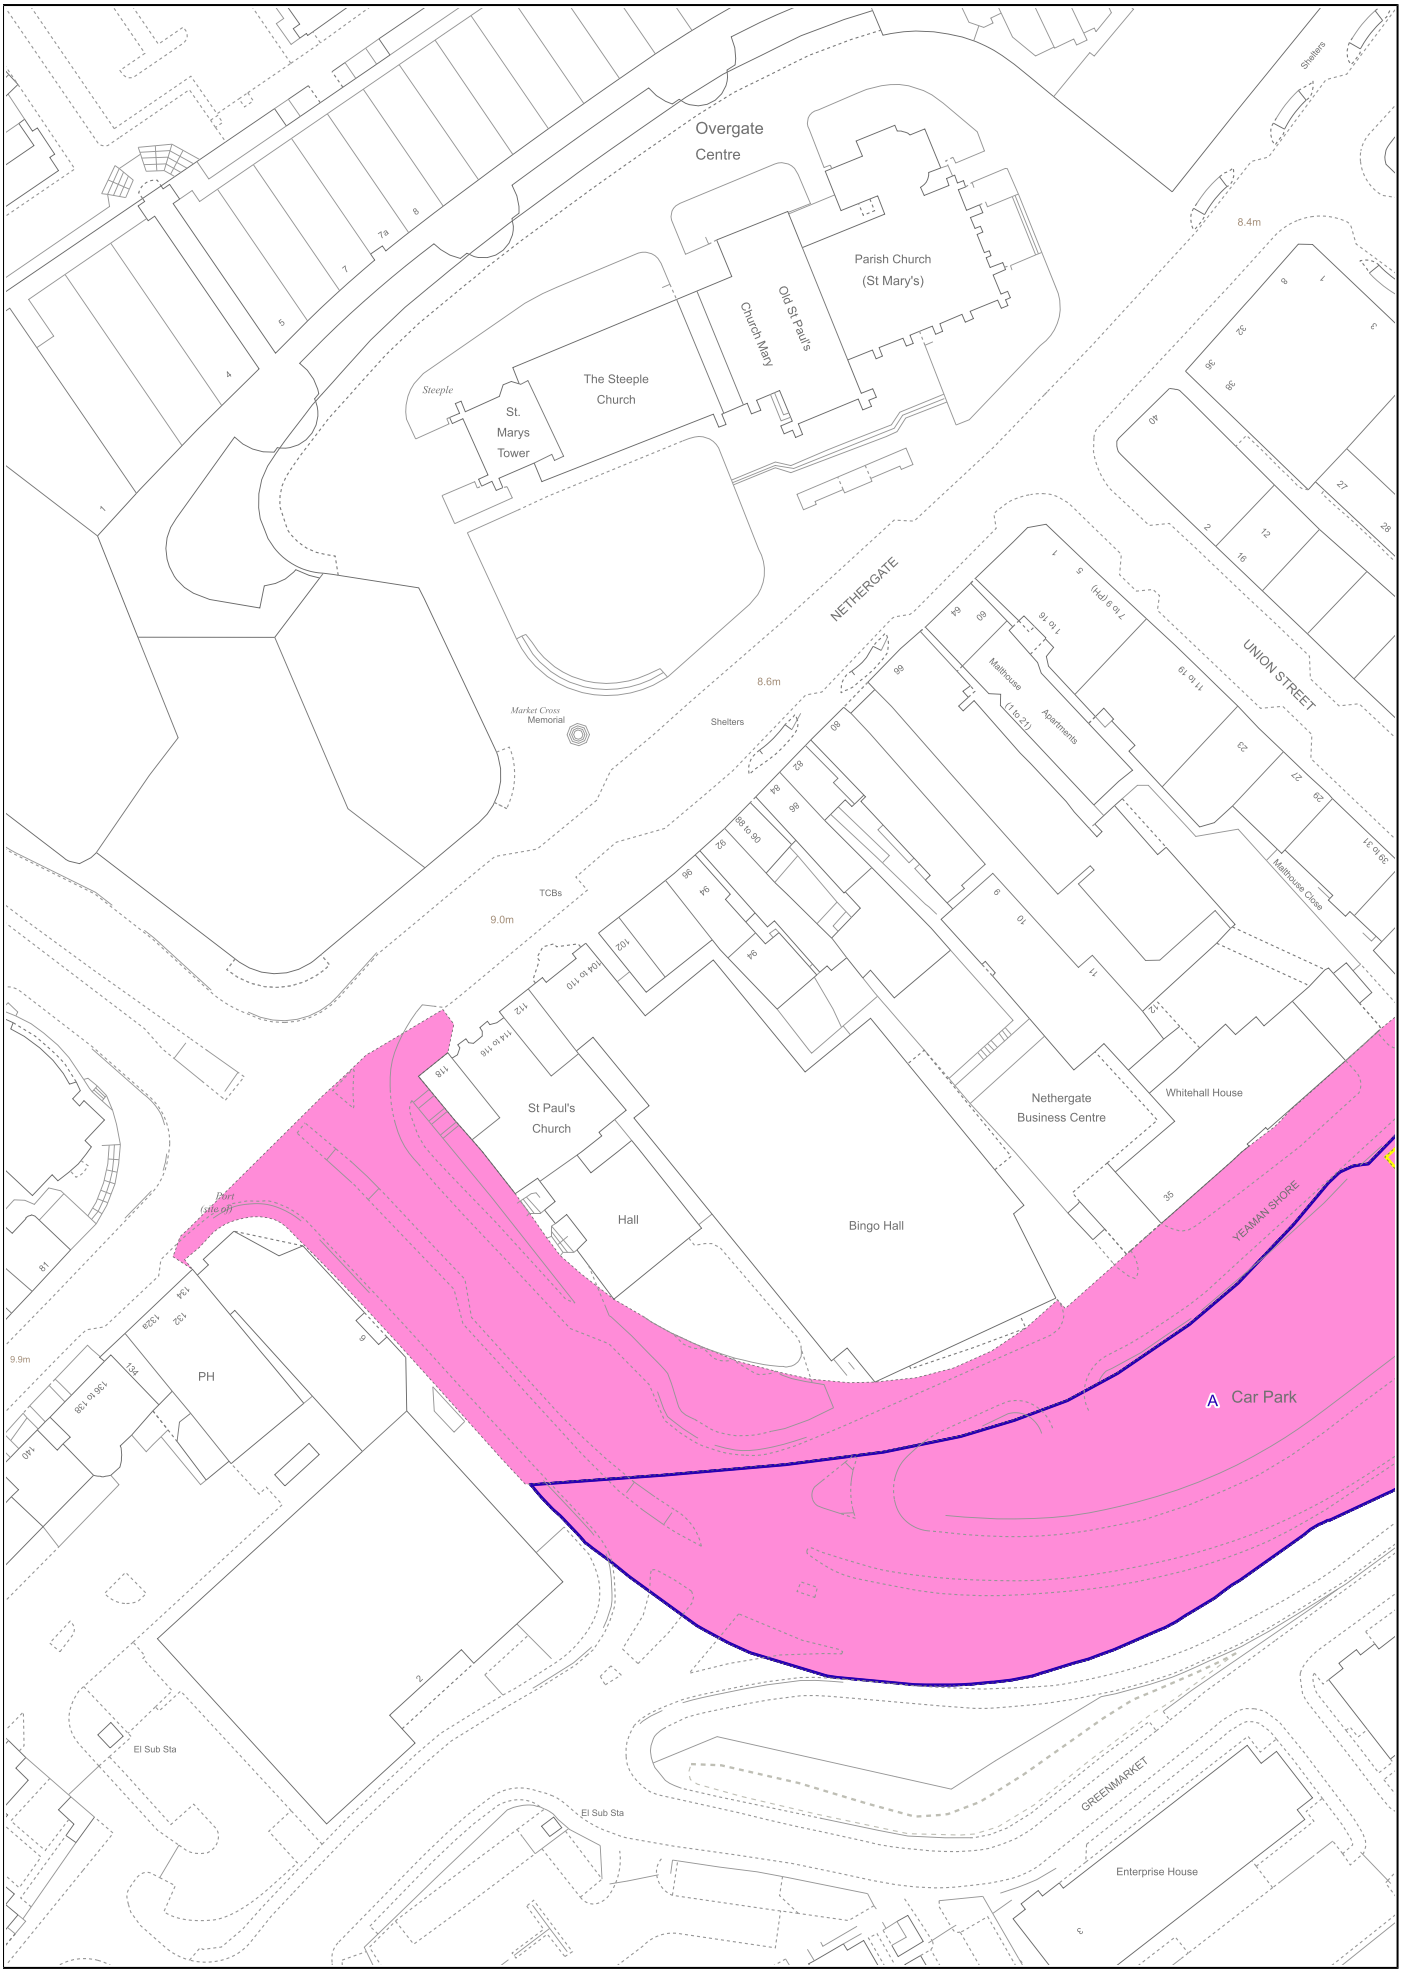
CROWN COPYRIGHT © This copy has been produced on 27/11/2025 with the authority of Ordnance Survey under Section 47 of the Copyright and Patents Act 1988. Unless there is a relevant exception to copyright, the copy must not be copied without prior permission of the copyright owner. OS Licence no AC0000820447.
This extract may contain Ordnance Survey features captured at other scales.

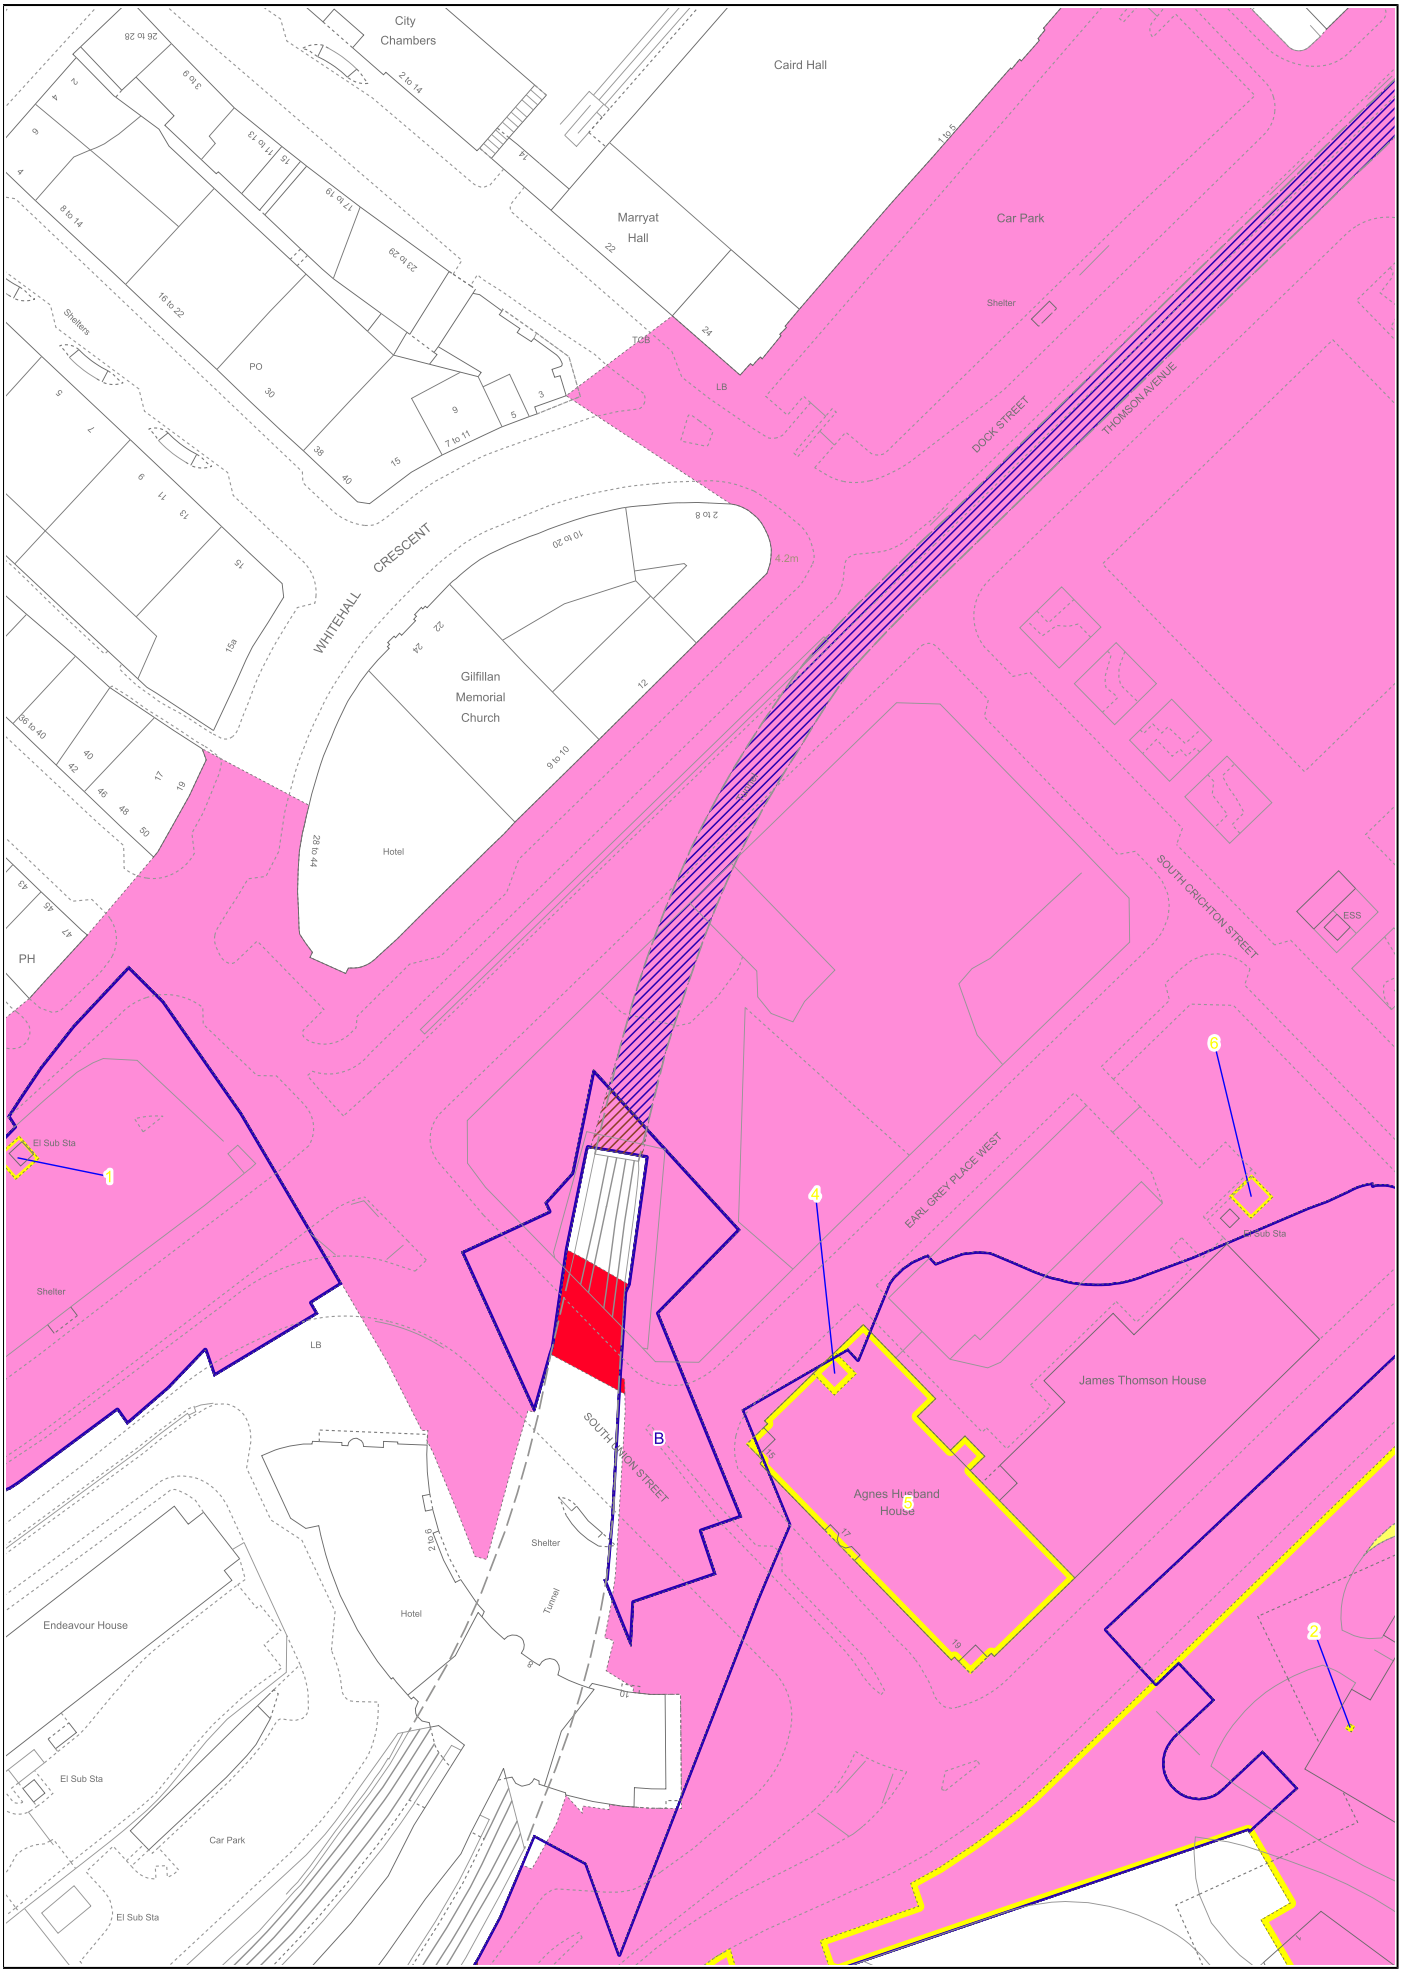



PETER STREET
MEADOWSIDE
MEADOW ENTRY
Cameron's Close
MURRAYGATE
COMMERCIAL STREET
Shelters
Line Of Posts
9.1m
Keiller Shopping Centre
RANKINE'S COURT
Campbell's Close
Grant's Close
Crooms Close
TCBs
Statues
HIGH STREET
CITY SQUARE
LBs
Fn
Post
ESS
Shelter
SEAGATE
PH
TCBs
5.2m
8.1m
9.2m
5.8m
Statue
DW
Castlehill
St Paul's
Cathedral
CASTLE STREET
Chy
St Andrews Brewing Co

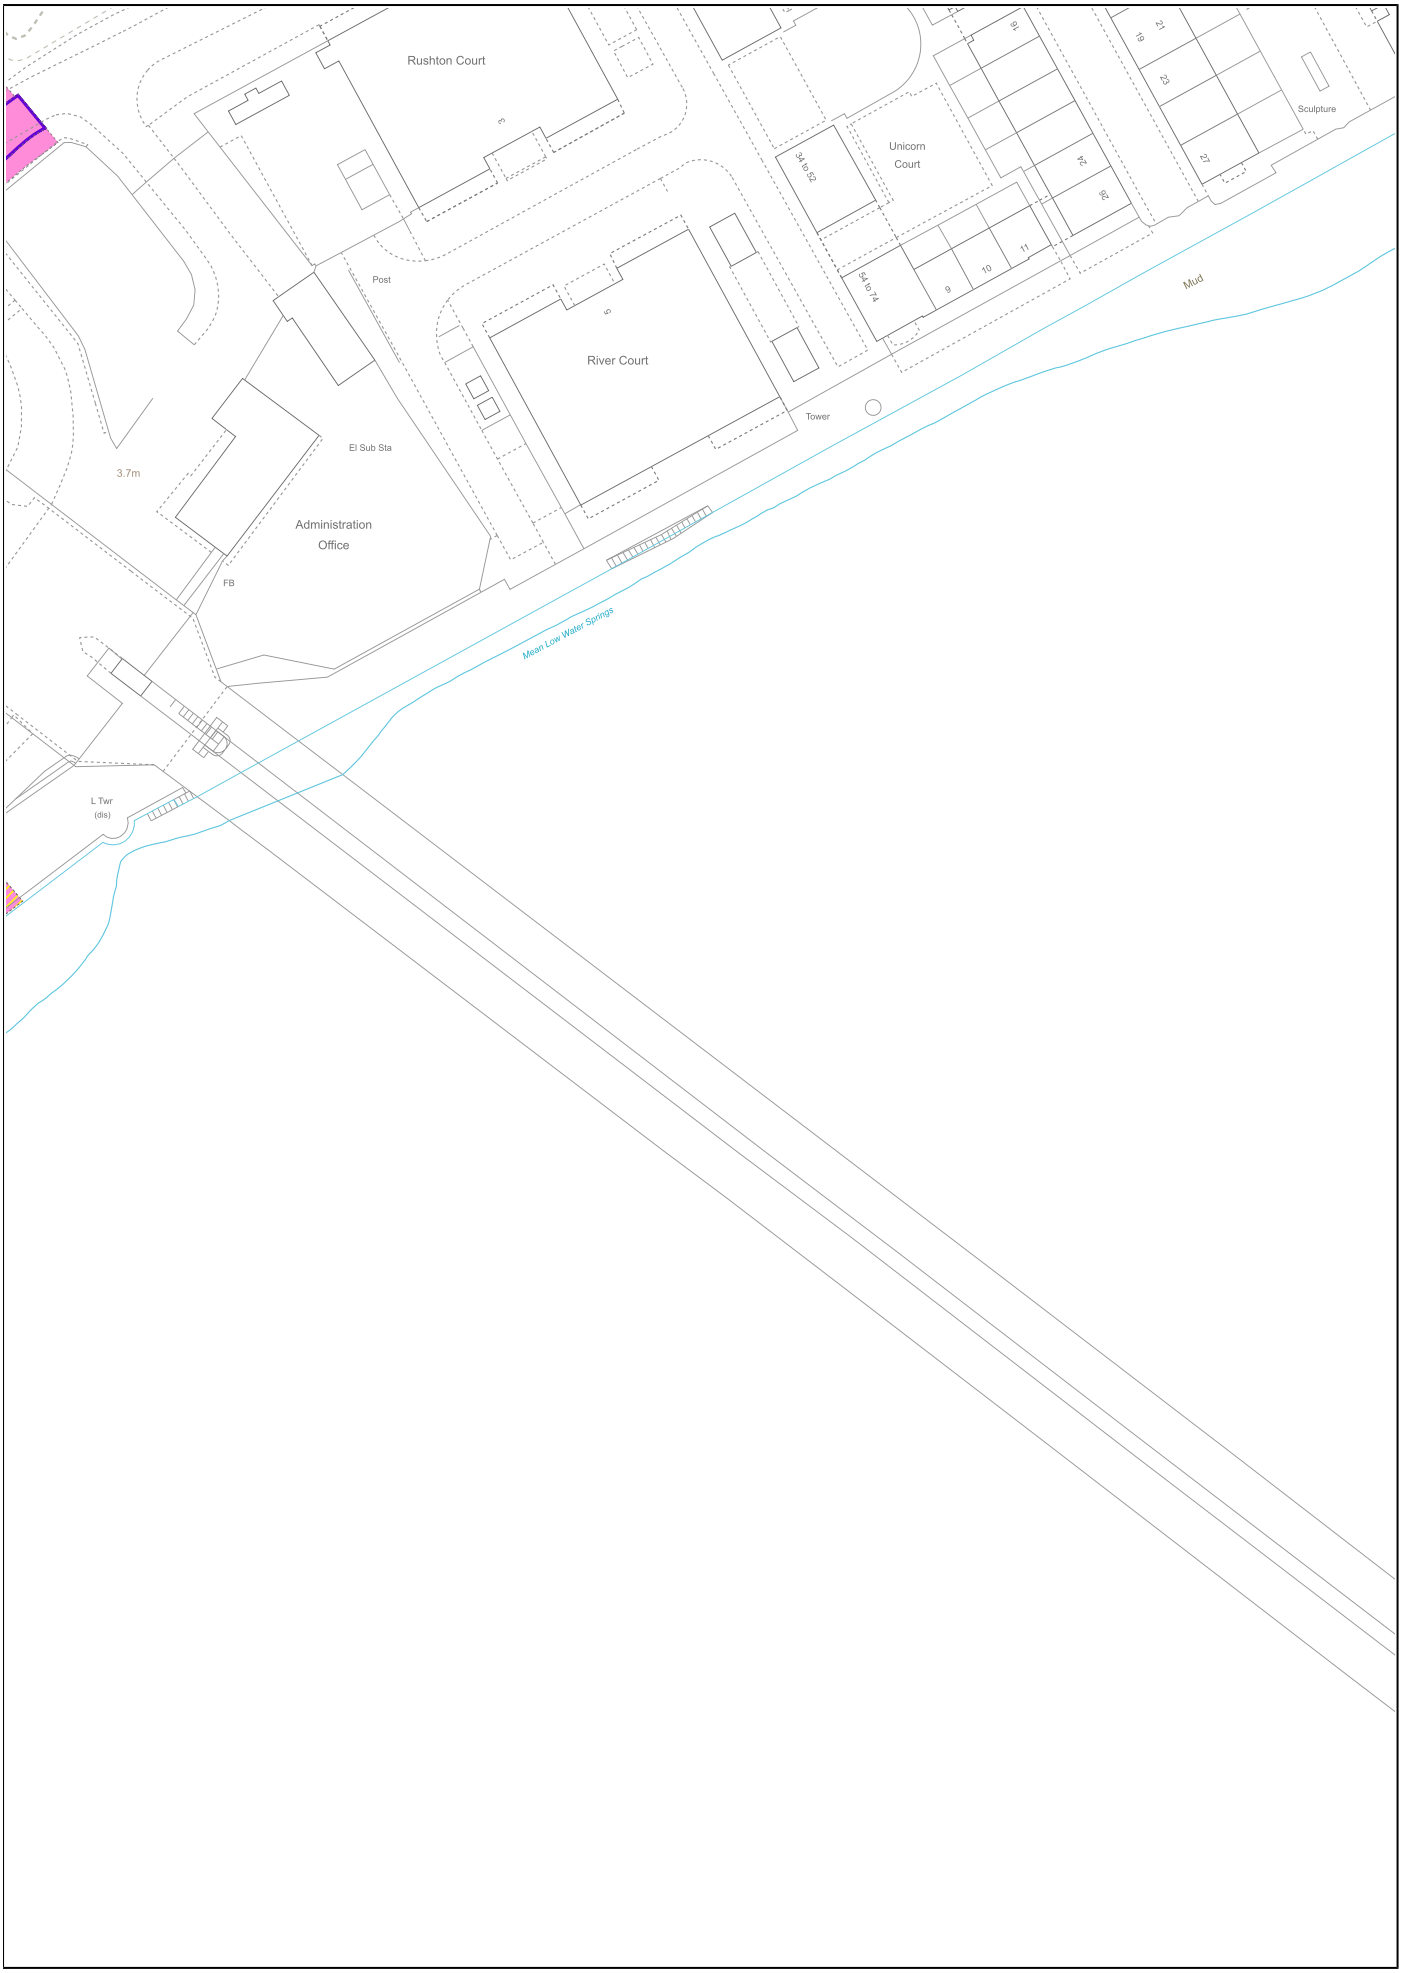

CANDLE LANE
ALLAN LANE
TRADES LANE
MARY ANN LANE
GELLATLY STREET
COMMERCIAL COURT
COMMERCIAL STREET
DOCK STREET
SOUTH COMMERCIAL STREET
Multi-storey Car Park
Hotel
Customs House
Harbour Chambers
Maritime House
Line Of Posts
4.0m
4.4m
4.1m
ESS
LB
FB

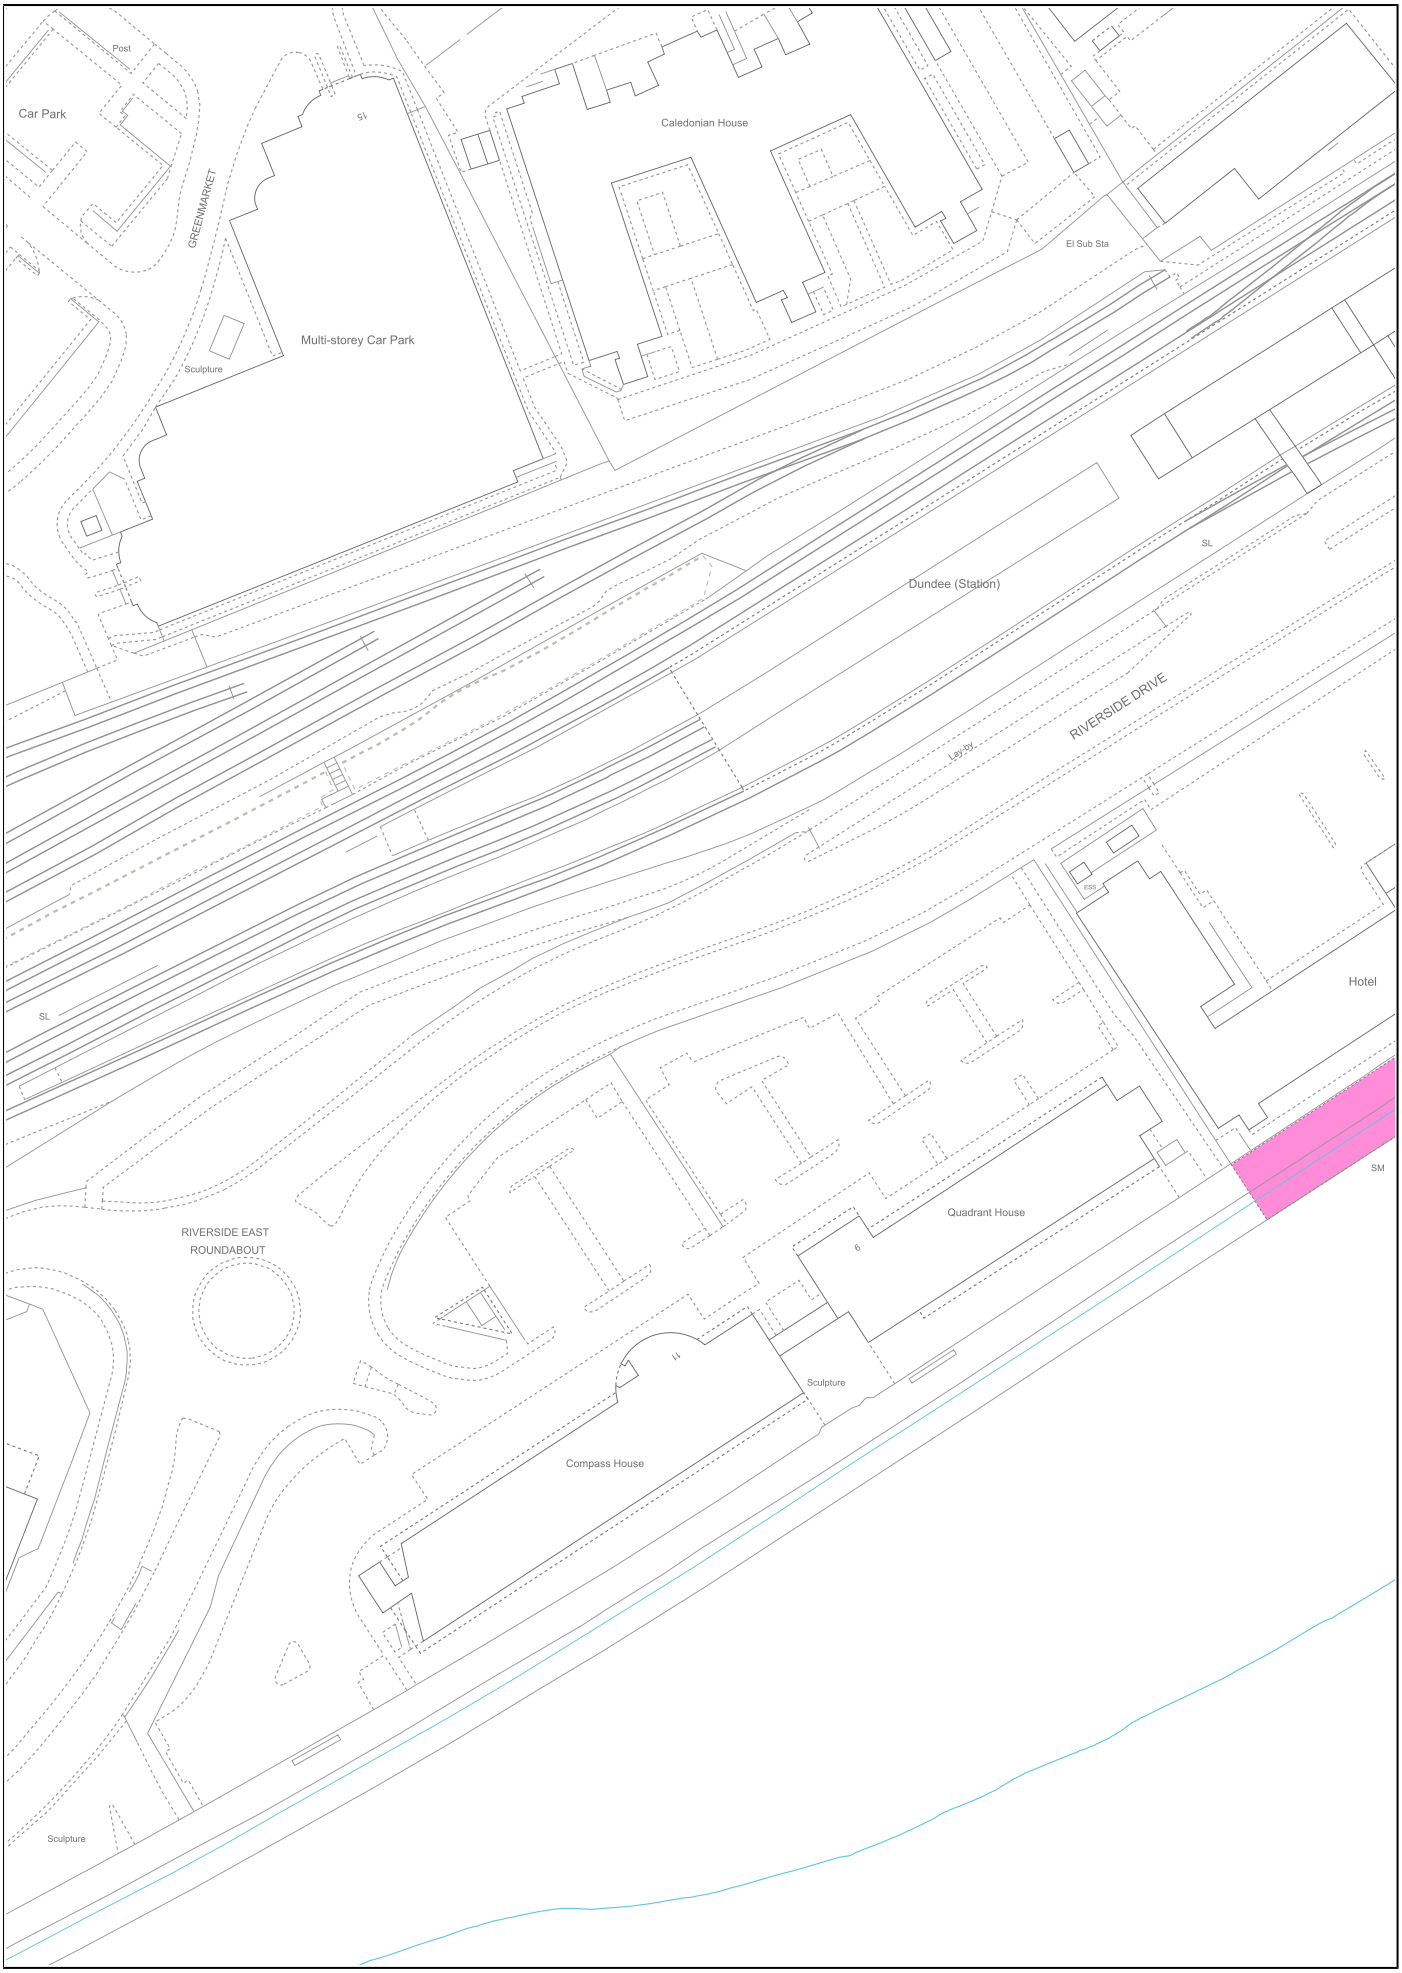

Car Park
Conveyor
Tanks
Tank
Conveyor
Hopper
ESS
CAMPERDOWN STREET
S Br
1a
1b
1c to 1d
3 to 4
5
6a
6b
7
9
10
11
12
14
15
16
17
18
19
20
21
22
23
25
FB
FB
Water Sports Centre
WEST VICTORIA DOCK ROAD
Hotel
C
ESS
Posts
CHANDLERS LANE
1
3
4
2 to 22
23
24
2 to B
10
11
14
15
17
Panmure
Court
Post

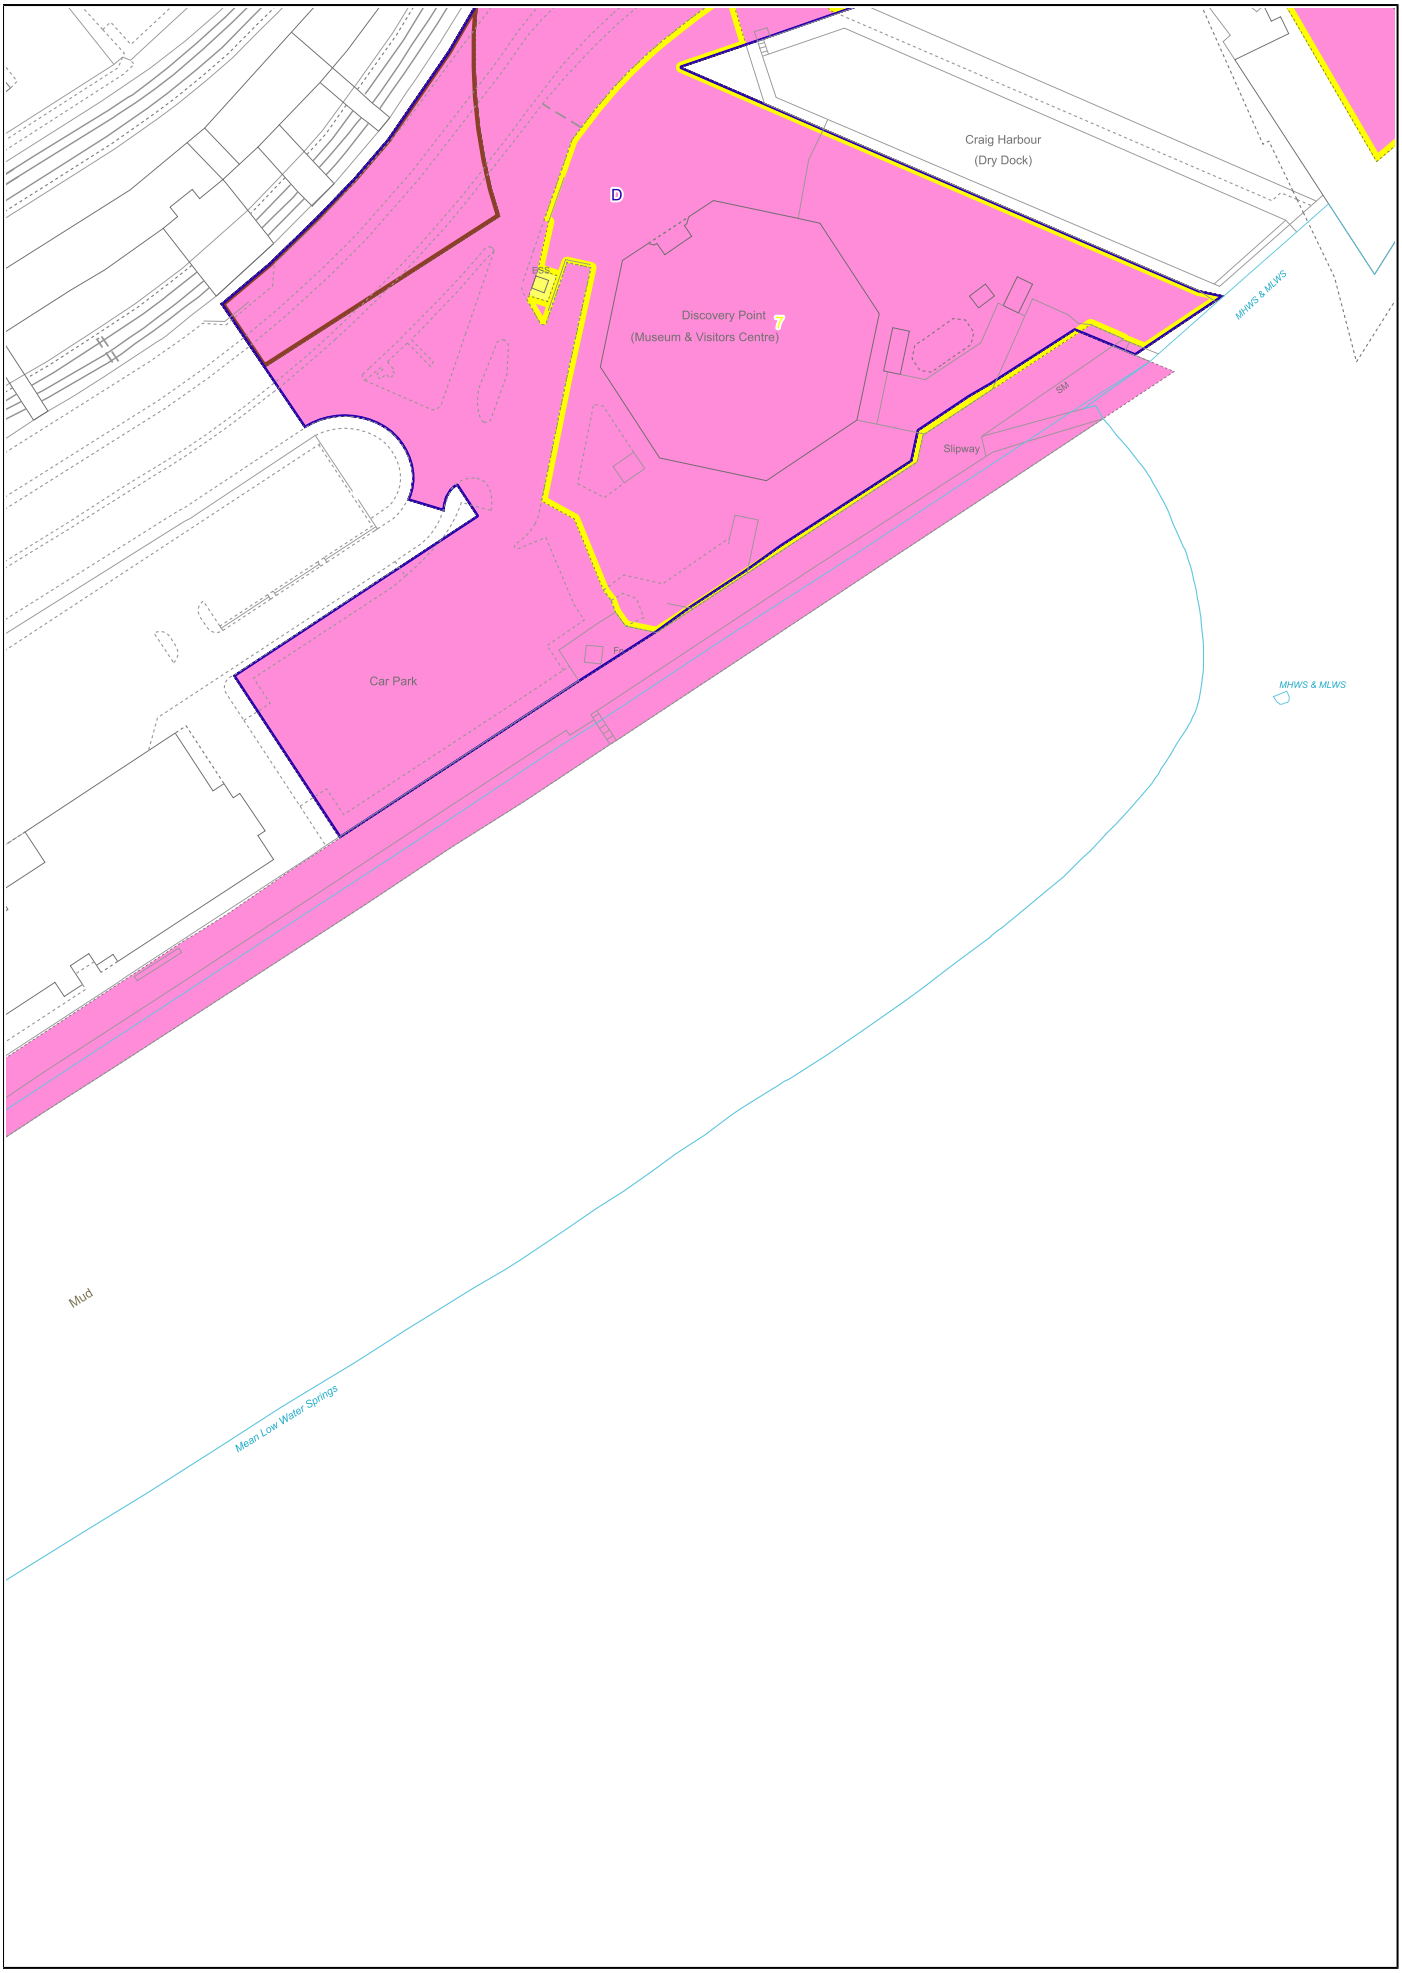

Overgate
Centre
Parish Church
(St Mary's)
Old St Paul's
Church Mary
The Steeple
Church
St.
Marys
Tower
Steeple
Market Cross
Memorial
Shelters
8.4m
8.6m
9.0m
9.9m
NETHERGATE
UNION STREET
Malthouse
Apartments
(1 to 21)
Malthouse Close
TCBs
St Paul's
Church
Hall
Bingo Hall
Nethergate
Business Centre
Whitehall House
YEAMAN SHORE
A Car Park
PH
El Sub Sta
El Sub Sta
GREENMARKET
Enterprise House


City Chambers
Caird Hall
Marryat Hall
Car Park
Shelter
TCB
LB
DOCK STREET
THOMSON AVENUE
WHITEHALL CRESCENT
Gilfillan Memorial Church
Hotel
PO
Shelters
4.2m
SOUTH CRICHTON STREET
ESS
PH
El Sub Sta
Shelter
LB
EARL GREY PLACE WEST
James Thomson House
Agnes Husband House
SOUTH UNION STREET
Shelter
Tunnel
Hotel
Endeavour House
El Sub Sta
Car Park
El Sub Sta
1
2
4
5
6
B


Whalers Lane
EARL GREY PLACE EAST
SOUTH CASTLE STREET
PATENT SLIPWAY
Slessor Gardens
Cycle
Hire Station
RIVERSIDE ESPLANADE
Mud
Monument
Travel Hub
Waterfront Place
Sculpture
Mud
Mean Low Water Springs
V & A Museum


Rushton Court
Unicorn Court
Sculpture
River Court
Post
El Sub Sta
3.7m
Administration Office
FB
Tower
Mud
Mean Low Water Springs
L Twr (dis)
34 to 52
54 to 74
16
19
21
23
27
24
28
9
10
11
5
3


Post
Car Park
GREENMARKET
Multi-storey Car Park
Sculpture
Caledonian House
El Sub Sta
Dundee (Station)
SL
RIVERSIDE DRIVE
Lay-by
ess
Hotel
SL
SM
Quadrant House
RIVERSIDE EAST
ROUNDABOUT
Sculpture
Compass House
Sculpture


Craig Harbour
(Dry Dock)
D
Discovery Point
(Museum & Visitors Centre)
7
FRP
MHWS & MLWS
SM
Slipway
Car Park
MHWS & MLWS
Mud
Mean Low Water Springs

